2013 AUG 19 PM 2:09

Bernard J. Youngblood
Wayne County Register of Deeds
August 19, 2013 02:10 PM
Inst:2013358497 EAS Pages:4
Liber:50970 Page:571



VEGETATION MANAGEMENT EASEMENT

On August 15, 2013, for good and valuable consideration, the receipt of which is hereby acknowledged, Muhammad Naeem, and Nudrat Razeeuddin, also known as Nudrat Naeem, husband and wife ("Grantor"), whose address is 23181 Westwood Drive, Brownstown Township, Michigan 48183, conveys and warrants to International Transmission Company, a Michigan corporation, of 27175 Energy Way, Novi, Michigan 48377 ("Grantee"), its successors and assigns, a permanent easement ("Easement") over, under, across and through a part of "Grantor's Land" referred to as the "Easement Area" and/or the "Easement Description," all of which are described on Exhibit "A" attached hereto.

1. **Purpose:** The purpose of this Easement is to provide Grantee with the perpetual right to enter at all times upon Grantor's Land to cut, trim, remove, destroy or otherwise control any or all trees, bushes or brush now or hereafter standing or growing within the Easement Area.

2. **Restoration:** Within a reasonable time after performing any work pursuant to this Easement, Grantee shall clean up the Easement Area in accordance with best management practices for utility rights of way.

3. **Limited Use; Nonuse:** Nonuse or limited use of the rights herein granted shall not prevent later use to the full extent herein conveyed.

4. **Original Grant of Easement:** Nothing contained in this Easement shall be construed as releasing or impairing any rights or privileges granted to Grantee or The Detroit Edison Company under any existing grant of easement ("Original Grant of Easement") relative to the Grantor's Land. To the extent this Easement grants rights and privileges to either Grantor or Grantee not granted in the Original Grant of Easement, the Original Grant of Easement is hereby amended to include the additional rights and privileges granted by this Easement. If, in any other way, any term, condition or provision of this Easement is inconsistent with or conflicts with one or more provisions of the Original Grant of Easement, the term, condition or provision of this Easement shall control, and to that extent, the Original Grant of Easement is hereby amended. The Original Grant of Easement, insofar as it may cover and relate to land other than Grantor's Land, shall remain in full force and effect in accordance with all of its terms, conditions and provisions.

5. **Damage Repair:** Grantee shall pay for any actual damage to Grantor's Land or Grantor's personal property resulting from Grantee's exercise of any of Grantee's rights under this Easement. Notwithstanding the foregoing, at no time shall Grantee be responsible for any damage to the extent that such damage results in whole, or in part, from Grantor's negligence. The term actual damage as used in this section is not intended to, nor does it, include damage to vegetation within the Easement Area as contemplated in paragraph 1.

6. **Successors:** This Easement runs with the land and binds and benefits Grantor's and Grantee's successors and assigns.

This Easement is exempt from real estate transfer tax pursuant to MCLA 207.505(f) and from State real estate transfer tax pursuant to the provisions of MCLA 207.526(f).

GRANTOR

M. Naeem
Muhammad Naeem

Nudrat Razeeuddin, a/k/a Nudrat Naeem

Acknowledged before me in Oakland County, Michigan, on this 15th day of August, 2013 by Muhammad Naeem, and Nudrat Razeeuddin, a/k/a Nudrat Naeem, husband and wife.


Dean F. Whitehead
DEAN F. WHITEHEAD Notary Public
Oakland County, Michigan
Acting in Oakland County, Michigan
My Commission Expires 09-14-2017

Drafted by:
Patricia Murphy (P61872)
ITC Holdings Corp.
27175 Energy Way
Novi, MI 48377

When recorded return to:
NSI Consulting & Development
24079 Research Drive
Farmington Hills, MI 48335

Exhibit "A"

BN-56 (NAEEM/RAZEEUDDIN)

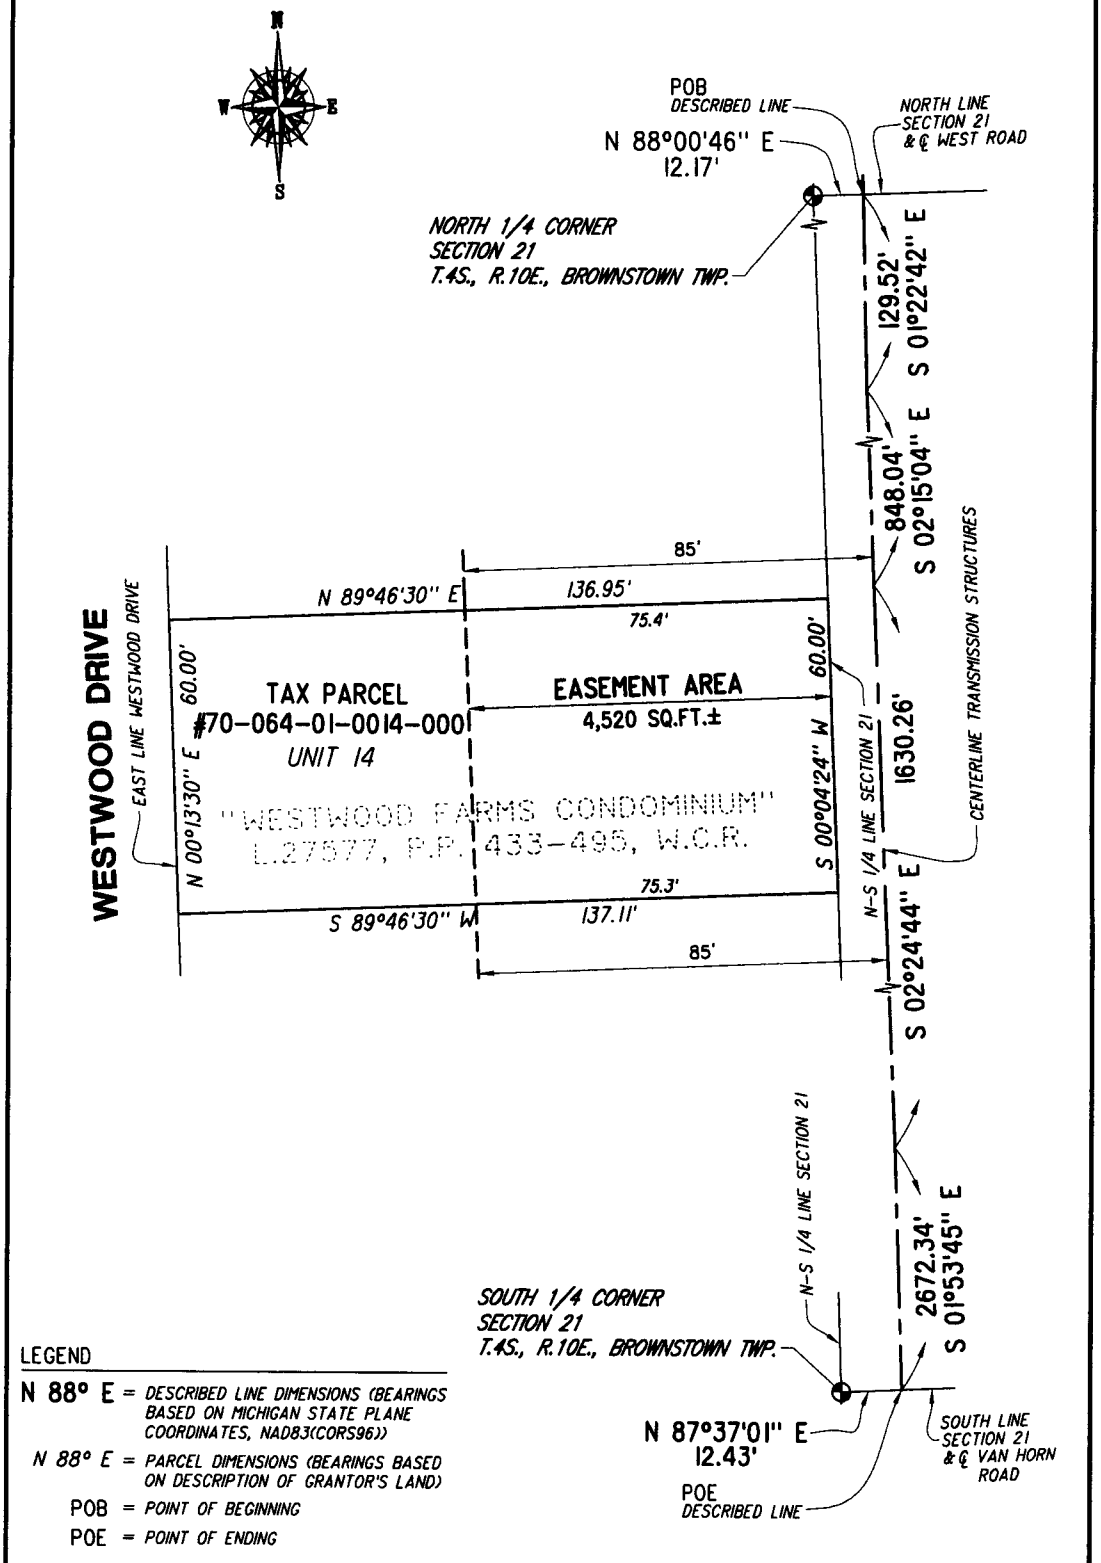

LEGEND

N 88° E = DESCRIBED LINE DIMENSIONS (BEARINGS BASED ON MICHIGAN STATE PLANE COORDINATES, NAD83(CORS96))

N 88° E = PARCEL DIMENSIONS (BEARINGS BASED ON DESCRIPTION OF GRANTOR'S LAND)

POB = POINT OF BEGINNING

POE = POINT OF ENDING

30 0 15 30 60

1 inch = 30 feet

REVISED 4/6/12
Sheet 1 of 2
8042.223 Easement Drawings.dwg

COPYRIGHT ©2012 McNEELY & LINCOLN ASSOCIATES, INC.

McNEELY&LINCOLN
Associates,Inc.
CIVIL ENGINEERING & LAND SURVEYING
PH. (734) 432-9777 FAX (734) 432-9786
37741 PEMBROKE, LIVONIA, MICHIGAN, 48152
WWW.MNLINC.COM

For	I.T.C.	Date	9/30/11
Scale	1"=30'	Drawn By	DP
Job No.	8042.223	Checked By	DW

Structures #951 - #1739

BN-56 (NAEEM/RAZEEUDDIN)

GRANTOR'S LAND

Unit 14, "Westwood Farms Condominium", according to the Master Deed recorded in Liber 27577, Pages 433 through 495, inclusive, Wayne County Records and designated as Wayne County Condominium Subdivision Plan Number 373, together with rights in general common elements and limited common elements, as set forth in the above-described Master Deed and as described in Act 59 of the Public Acts of 1978 as amended.

Tax Parcel #70-064-01-0014-000

EASEMENT DESCRIPTION

All that part of the above-described Grantor's Land which lies Easterly of a line eighty-five (85.00) feet Westerly of and parallel with the following described line:

Commencing at the North 1/4 corner of Section 21, Town 4 South, Range 10 East;
thence North 88 degrees 00 minutes 46 seconds East, along the North line of Section 21, also the centerline of West Road, 12.17 feet to the **Point of Beginning** of said line;
thence South 01 degree 22 minutes 42 seconds East 129.52 feet;
thence South 02 degrees 15 minutes 04 seconds East 848.04 feet;
thence South 02 degrees 24 minutes 44 seconds East 1630.26 feet;
thence South 01 degree 53 minutes 45 seconds East 2672.34 feet to the **Point of Ending** of said line, said point lying distant North 87 degrees 37 minutes 01 second East, along the South line of Section 21, also the centerline of Van Horn Road, 12.43 feet from the South 1/4 corner of Section 21.

Grantor's Land more commonly known as: 23181 Westwood Drive, Brownstown Township

REVISED 4/6/12
Sheet 2 of 2
8042.223 Easement Drawings.dwg
COPYRIGHT ©2012 McNEELY & LINCOLN ASSOCIATES, INC.

McNEELY&LINCOLN
Associates,Inc.
CIVIL ENGINEERING & LAND SURVEYING
PH. (734) 432-9777 FAX (734) 432-9786
37741 PEMBROKE, LIVONIA, MICHIGAN, 48152
WWW.MNLINC.COM

For	I.T.C.	Date	9/30/11
Scale	NONE	Drawn By	DP
Job No.	8042.223	Checked By	DW

Structures #951 - #1739